


Begane grond

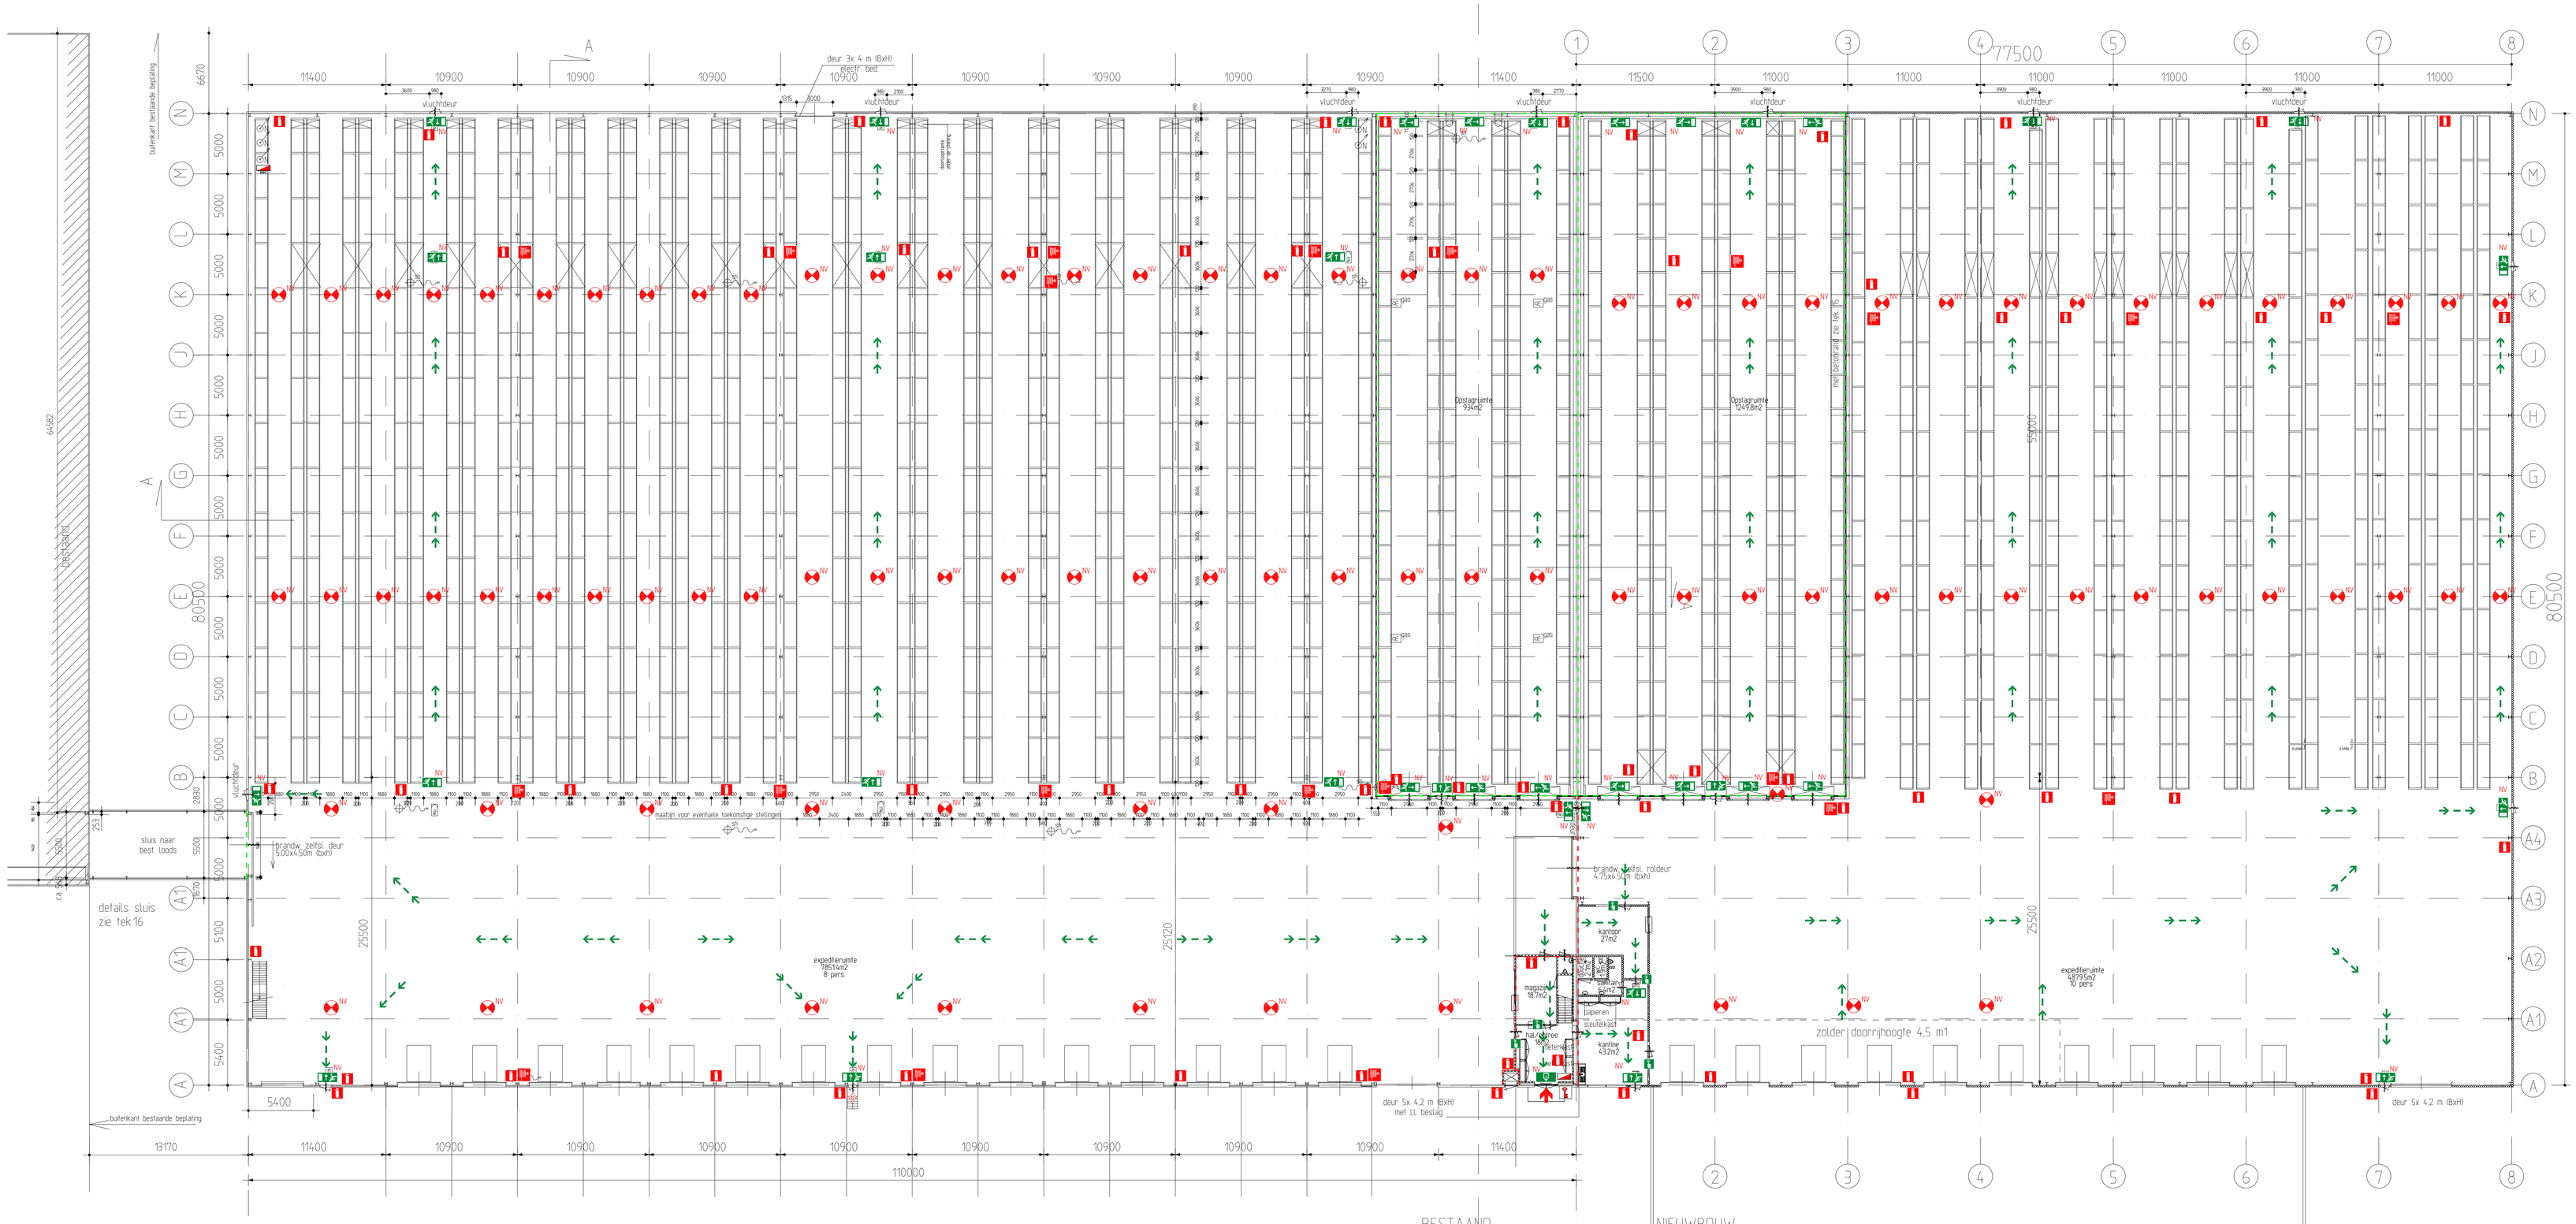


Verdieping

Vloerhoogte

Maaiveld: 0.28-peil

Beganegrond: peil=0 (=0.96+NAP)

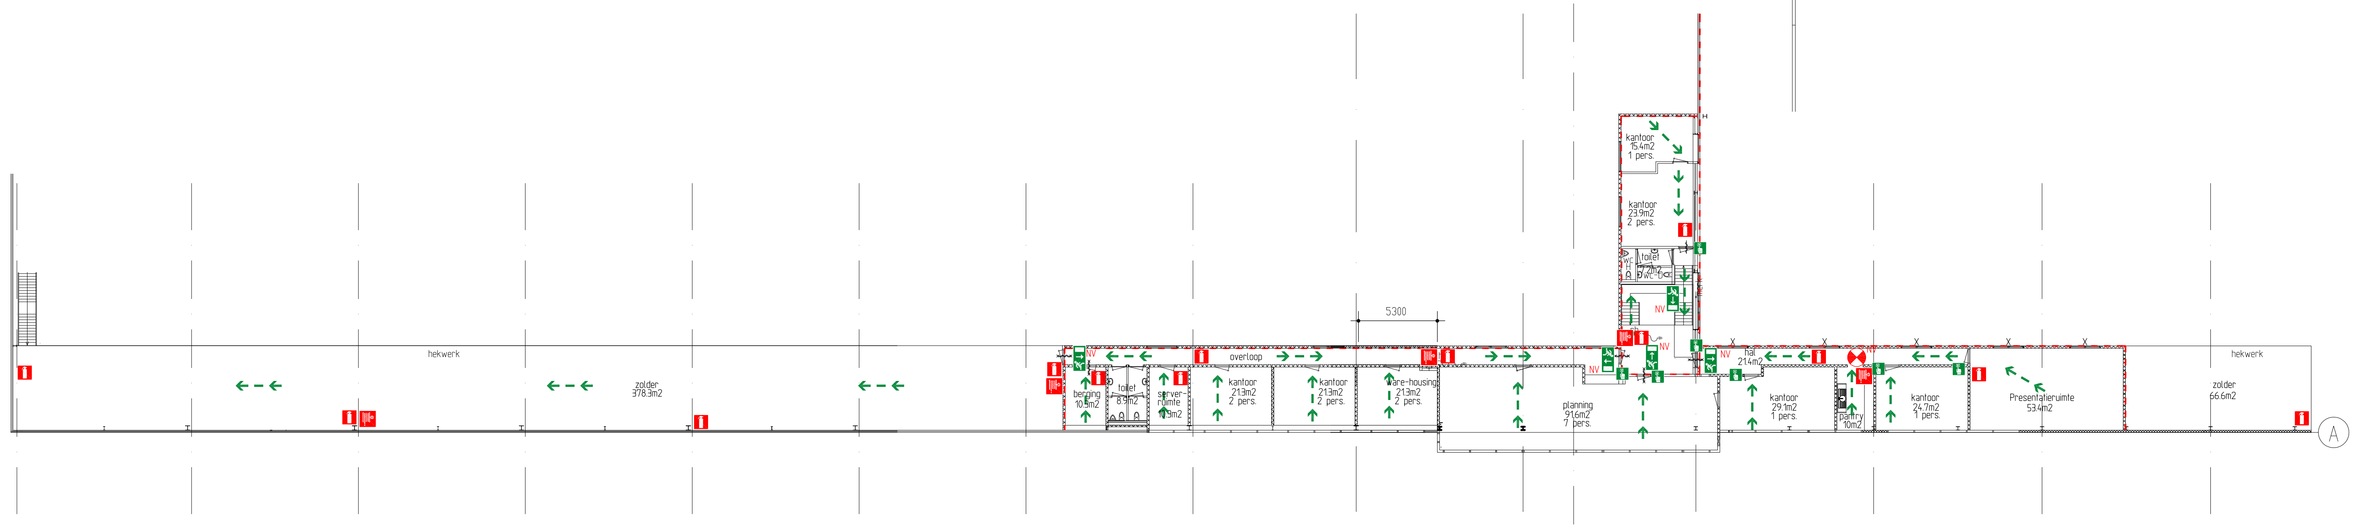Verdieping: 4.98+peil

Gebruiksoppervlak (GO)

Beganegrond: 150816 m2

Verdieping: 894.2 m2

Maximaal aantal personen

Beganegrond: 18 personen

Verdieping: 18 personen

Symbolen Gebruiksbesluit NEN1414

- 30 min brandwerende scheiding
- 60 min brandwerende scheiding
- rookwerende scheiding
- vluchtroute
- Brandwerende deur
- Brandwerende zelfsluitende deur
- Zelfsluitende deur
- Noodontgrendeling van deur
- Normale uitgang
- Vluchtrichting
- Brandmeldcentrale
- Brandweerpaneel
- Brandslanghaspel
- Brandblusser
- Sleutelkluis
- Brandweeringang
- Overige ingang
- Noodverlichting

| WIJZIGING | DATUM | OMSCHRIJVING WIJZIGINGEN | GETEKEND | CONTROLE |
|---|---|---|---|---|

OPMERKINGEN

CONCEPT

| | | |
|---|---|---|
| GETEKEND | M. Slob | AutoCAD 2009 |
| CONTROLE | R. Kruijer | DATUM 07-08-09 |
| SCHAAL | 1:200 | MAATSTAKEN mm |

VAN DER WIEL PLANONTWIKKELING BV

Heerpaal 11
7006 AJ DRACHTEN
Postbus 108
7200 AC DRACHTEN
Tel. 0512-566291
Fax. 0512-566211
info@vanderwiel.nl
www.vanderwiel.nl

OPDRACHTGEVER: Drenth Transport te Hoogezand

PROJECT: Uitbreiding loods Techniekweg te Hoogezand

OMSCHRIJVING: Plattegronden t.b.v. Gebruiksvergunning

| PROJECTNUMMER | TEKENINGNUMMER | BLAD 1 UIT 1 |
|---|---|---|
| I000485 | 4522_V003 | A0 |

©Het copyright van deze tekening behoort toe aan Van der Wiel Planontwikkeling BV